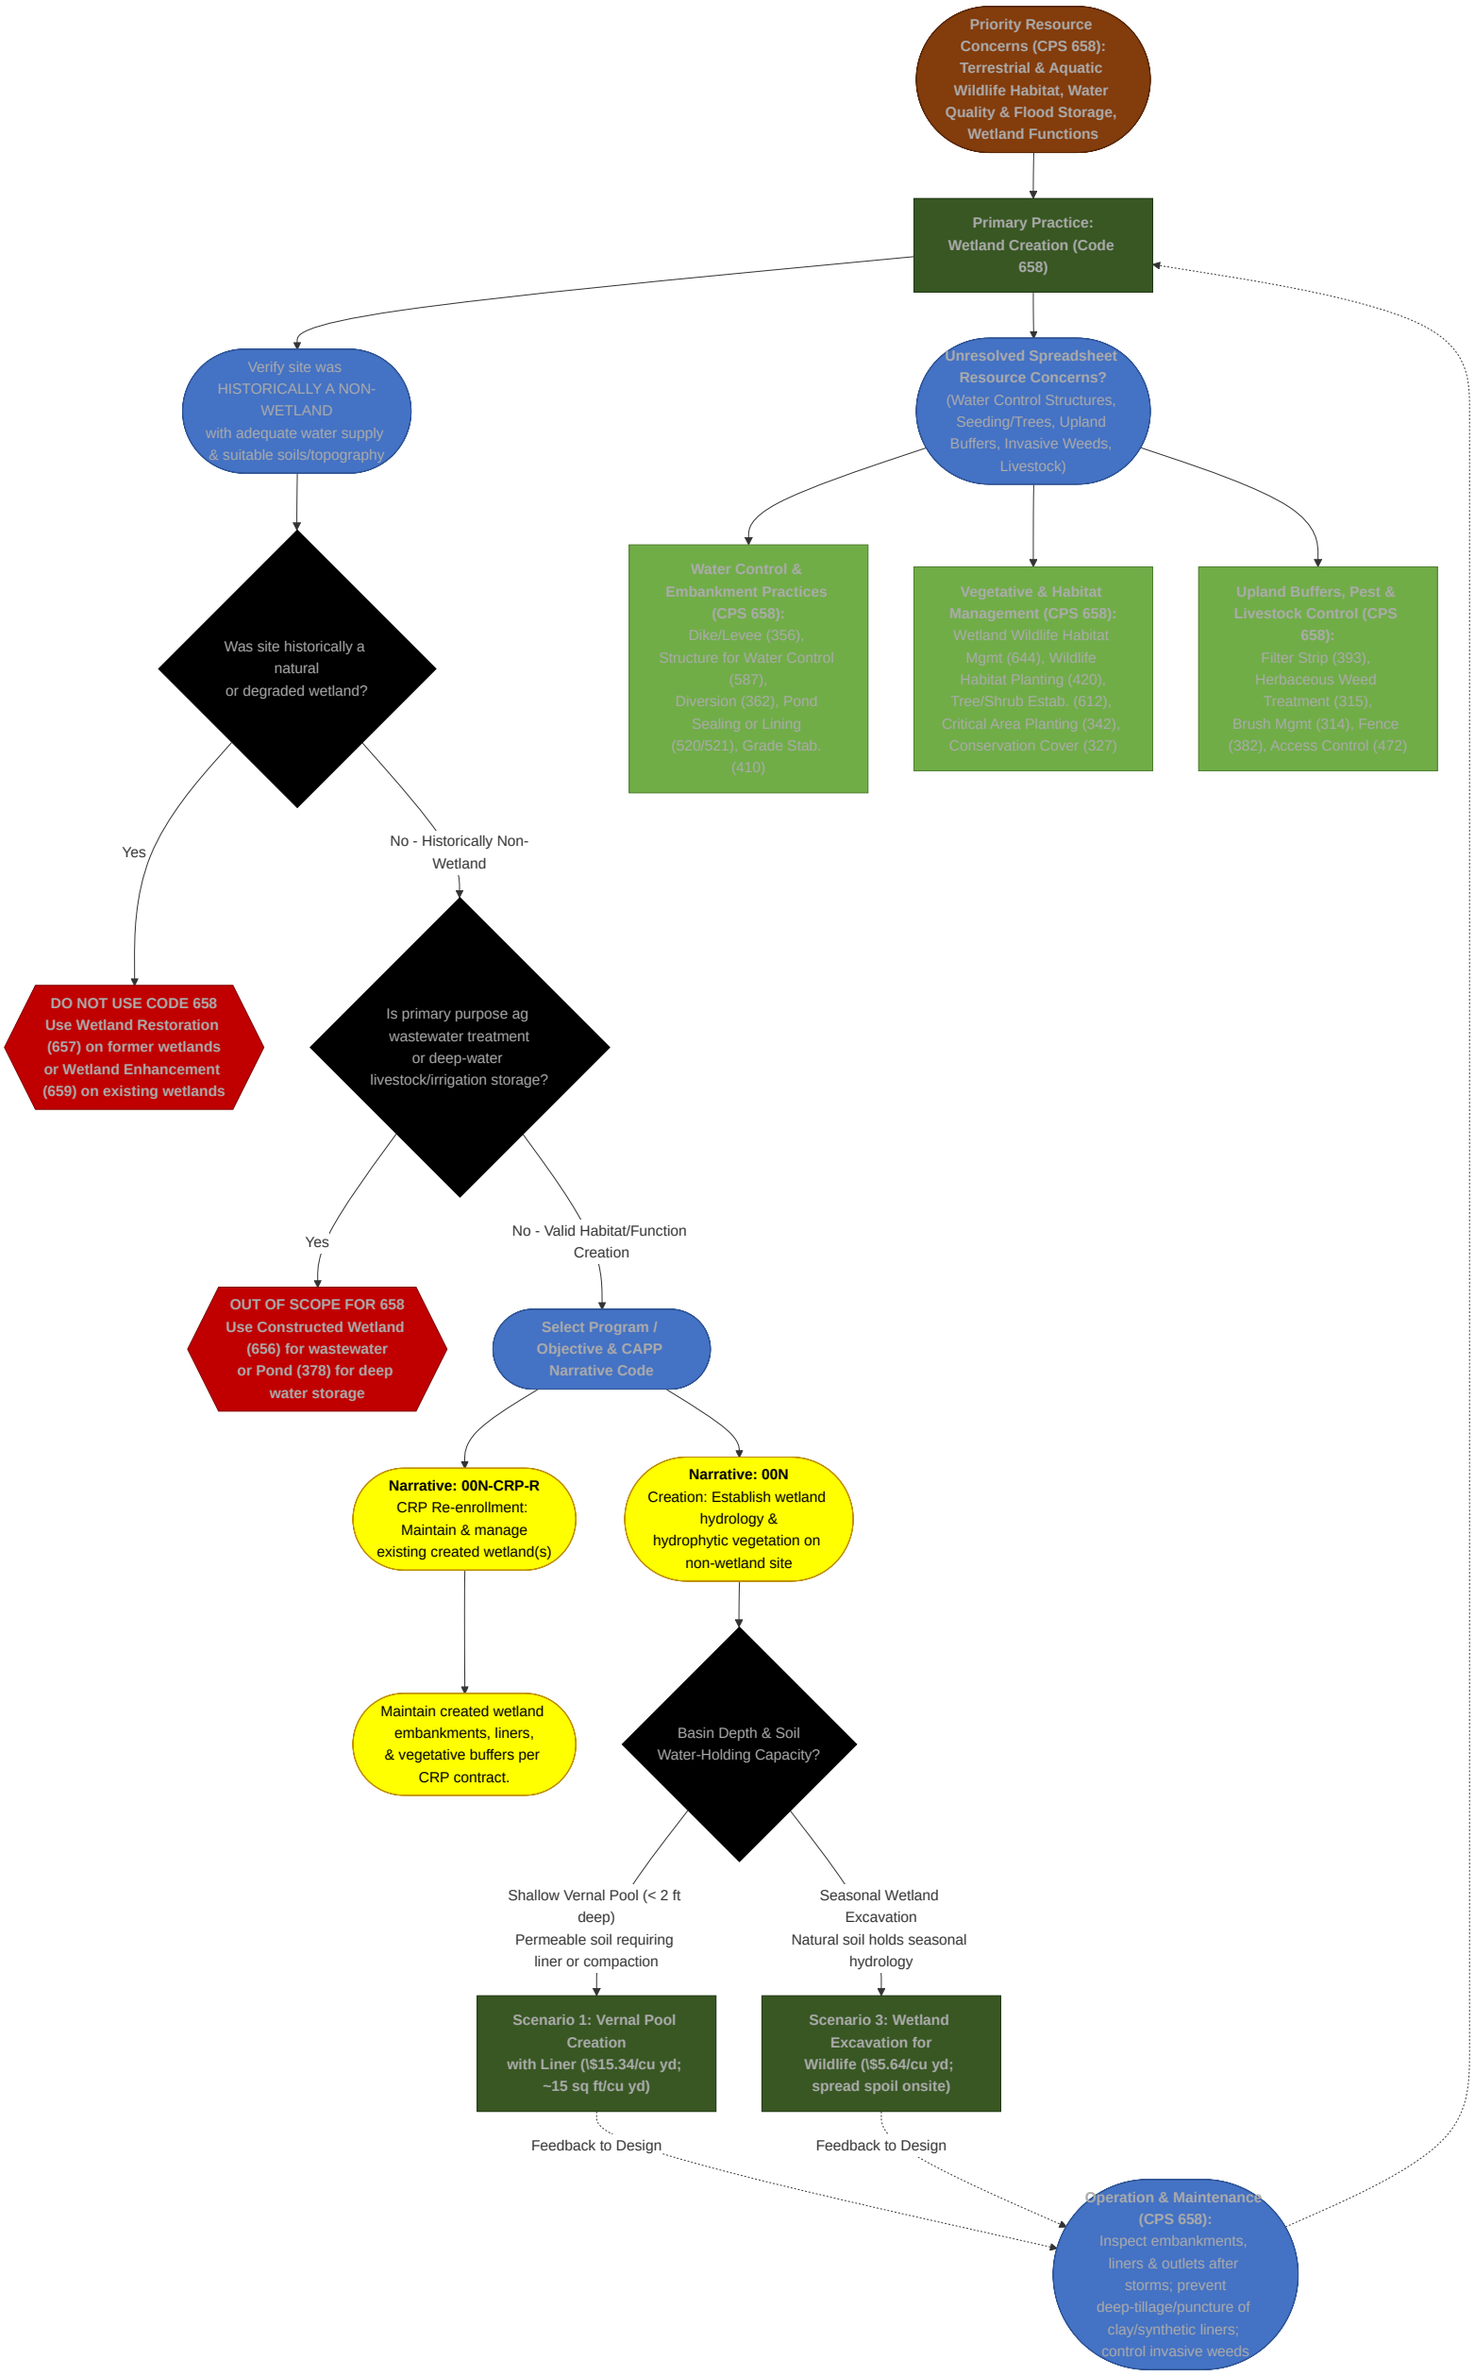

Priority Resource Concerns (CPS 658): Terrestrial & Aquatic Wildlife Habitat, Water Quality & Flood Storage, Wetland Functions
Primary Practice: Wetland Creation (Code 658)
Verify site was HISTORICALLY A NON-WETLAND with adequate water supply & suitable soils/topography
Unresolved Spreadsheet Resource Concerns? (Water Control Structures, Seeding/Trees, Upland Buffers, Invasive Weeds, Livestock)
Water Control & Embankment Practices (CPS 658): Dike/Levee (356), Structure for Water Control (587), Diversion (362), Pond Sealing or Lining (520/521), Grade Stab. (410)
Vegetative & Habitat Management (CPS 658): Wetland Wildlife Habitat Mgmt (644), Wildlife Habitat Planting (420), Tree/Shrub Estab. (612), Critical Area Planting (342), Conservation Cover (327)
Upland Buffers, Pest & Livestock Control (CPS 658): Filter Strip (393), Herbaceous Weed Treatment (315), Brush Mgmt (314), Fence (382), Access Control (472)
Was site historically a natural or degraded wetland?
Yes
No - Historically Non-Wetland
DO NOT USE CODE 658 Use Wetland Restoration (657) on former wetlands or Wetland Enhancement (659) on existing wetlands
Is primary purpose ag wastewater treatment or deep-water livestock/irrigation storage?
Yes
No - Valid Habitat/Function Creation
OUT OF SCOPE FOR 658 Use Constructed Wetland (656) for wastewater or Pond (378) for deep water storage
Select Program / Objective & CAPP Narrative Code
Narrative: 00N-CRP-R CRP Re-enrollment: Maintain & manage existing created wetland(s)
Narrative: 00N Creation: Establish wetland hydrology & hydrophytic vegetation on non-wetland site
Maintain created wetland embankments, liners, & vegetative buffers per CRP contract.
Basin Depth & Soil Water-Holding Capacity?
Shallow Vernal Pool (< 2 ft deep) Permeable soil requiring liner or compaction
Seasonal Wetland Excavation Natural soil holds seasonal hydrology
Scenario 1: Vernal Pool Creation with Liner (\$15.34/cu yd; ~15 sq ft/cu yd)
Scenario 3: Wetland Excavation for Wildlife (\$5.64/cu yd; spread spoil onsite)
Feedback to Design
Feedback to Design
Operation & Maintenance (CPS 658): Inspect embankments, liners & outlets after storms; prevent deep-tillage/puncture of clay/synthetic liners; control invasive weeds